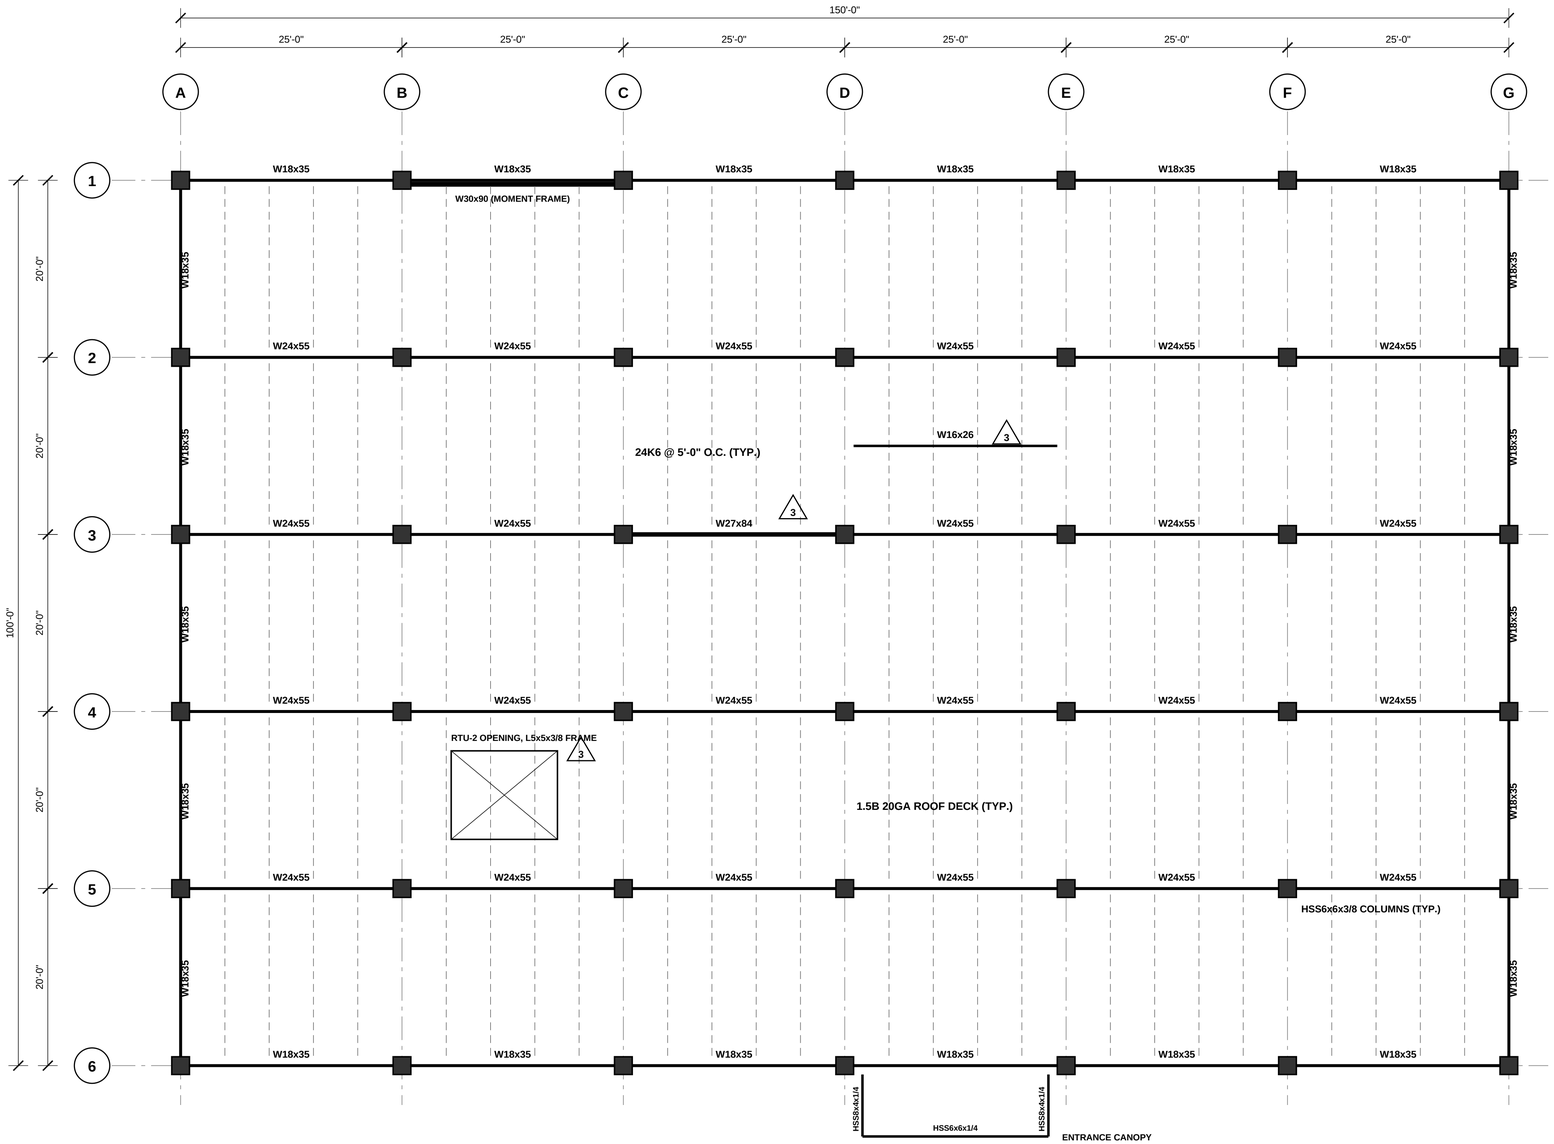

1 ROOF FRAMING PLAN

SCALE: 1/8" = 1'-0"

FRAMING NOTES

1. STRUCTURAL STEEL: W SHAPES ASTM A992; HSS ASTM A500 GR. C.
2. ANGLES, CHANNELS AND PLATES: ASTM A36.
3. T/STEEL EL. 126'-0" U.N.O.
4. JOISTS: SJI K-SERIES, BRIDGING PER SJI.
5. ROOF DECK: 1.5" TYPE B, 20 GA, GALVANIZED.
6. BEAM CONNECTIONS: SEE 1/S2.01.

MEMBER LEGEND

W24x55 INTERIOR GIRDER
W18x35 PERIMETER BEAM
W30x90 MOMENT FRAME BEAM
HSS6x6x3/8 COLUMN

NORTHPOINT
STRUCTURAL ENGINEERS
1200 Harbor Way, Suite 400

PROJECT

RIVERSIDE
DISTRIBUTION CENTER
4410 Industrial Parkway

REVISIONS

1	ISSUED FOR BID	03/14/2026
2	ADDENDUM 1	04/02/2026
3	ADDENDUM 2	05/06/2026

PROJECT NO. 2026-118
DATE 05/06/2026
DRAWN JRM
CHECKED KLT

SHEET TITLE

ROOF FRAMING PLAN

SHEET NUMBER

S1.02