

NORTHPOINTSTRUCTURAL ENGINEERS
1200 Harbor Way, Suite 400

PROJECT

**RIVERSIDE
DISTRIBUTION CENTER**

4410 Industrial Parkway


REVISIONS

1	ISSUED FOR BID	03/14/2026
2	ADDENDUM 1	04/02/2026

RIVERSIDE DISTRIBUTION CENTER

4410 INDUSTRIAL PARKWAY

CONSTRUCTION DOCUMENTS - ISSUED FOR BID

 **DRAWING INDEX**

G0.01	COVER SHEET
S1.01	FOUNDATION PLAN
S1.02	ROOF FRAMING PLAN
S2.01	STRUCTURAL SECTIONS AND DETAILS
A1.01	FIRST FLOOR PLAN
M1.01	MECHANICAL AND PLUMBING PLAN
E1.01	ELECTRICAL LIGHTING PLAN

PROJECT DATA

BUILDING AREA: 15,000 SF (150'-0" x 100'-0")
CONSTRUCTION TYPE: II-B, STEEL FRAME
ROOF: 1.5B 20GA METAL DECK ON 24K6 JOISTS
FOUNDATIONS: SPREAD AND CONTINUOUS FOOTINGS
SLAB ON GRADE: 6" CONCRETE, 4000 PSI

PROJECT NO.

2026-118

DATE

04/02/2026

DRAWN

JRM

CHECKED

KLT

SHEET TITLE

COVER SHEET

SHEET NUMBER

G0.01

NORTHPOINT

STRUCTURAL ENGINEERS
1200 Harbor Way, Suite 400

PROJECT

RIVERSIDE
DISTRIBUTION CENTER
4410 Industrial Parkway

REVISIONS

1	ISSUED FOR BID	03/14/2026
2	ADDENDUM 1	04/02/2026

PROJECT NO.

2026-118

DATE

04/02/2026

DRAWN

JRM

CHECKED


KLT

SHEET TITLE

FOUNDATION PLAN

SHEET NUMBER

S1.01

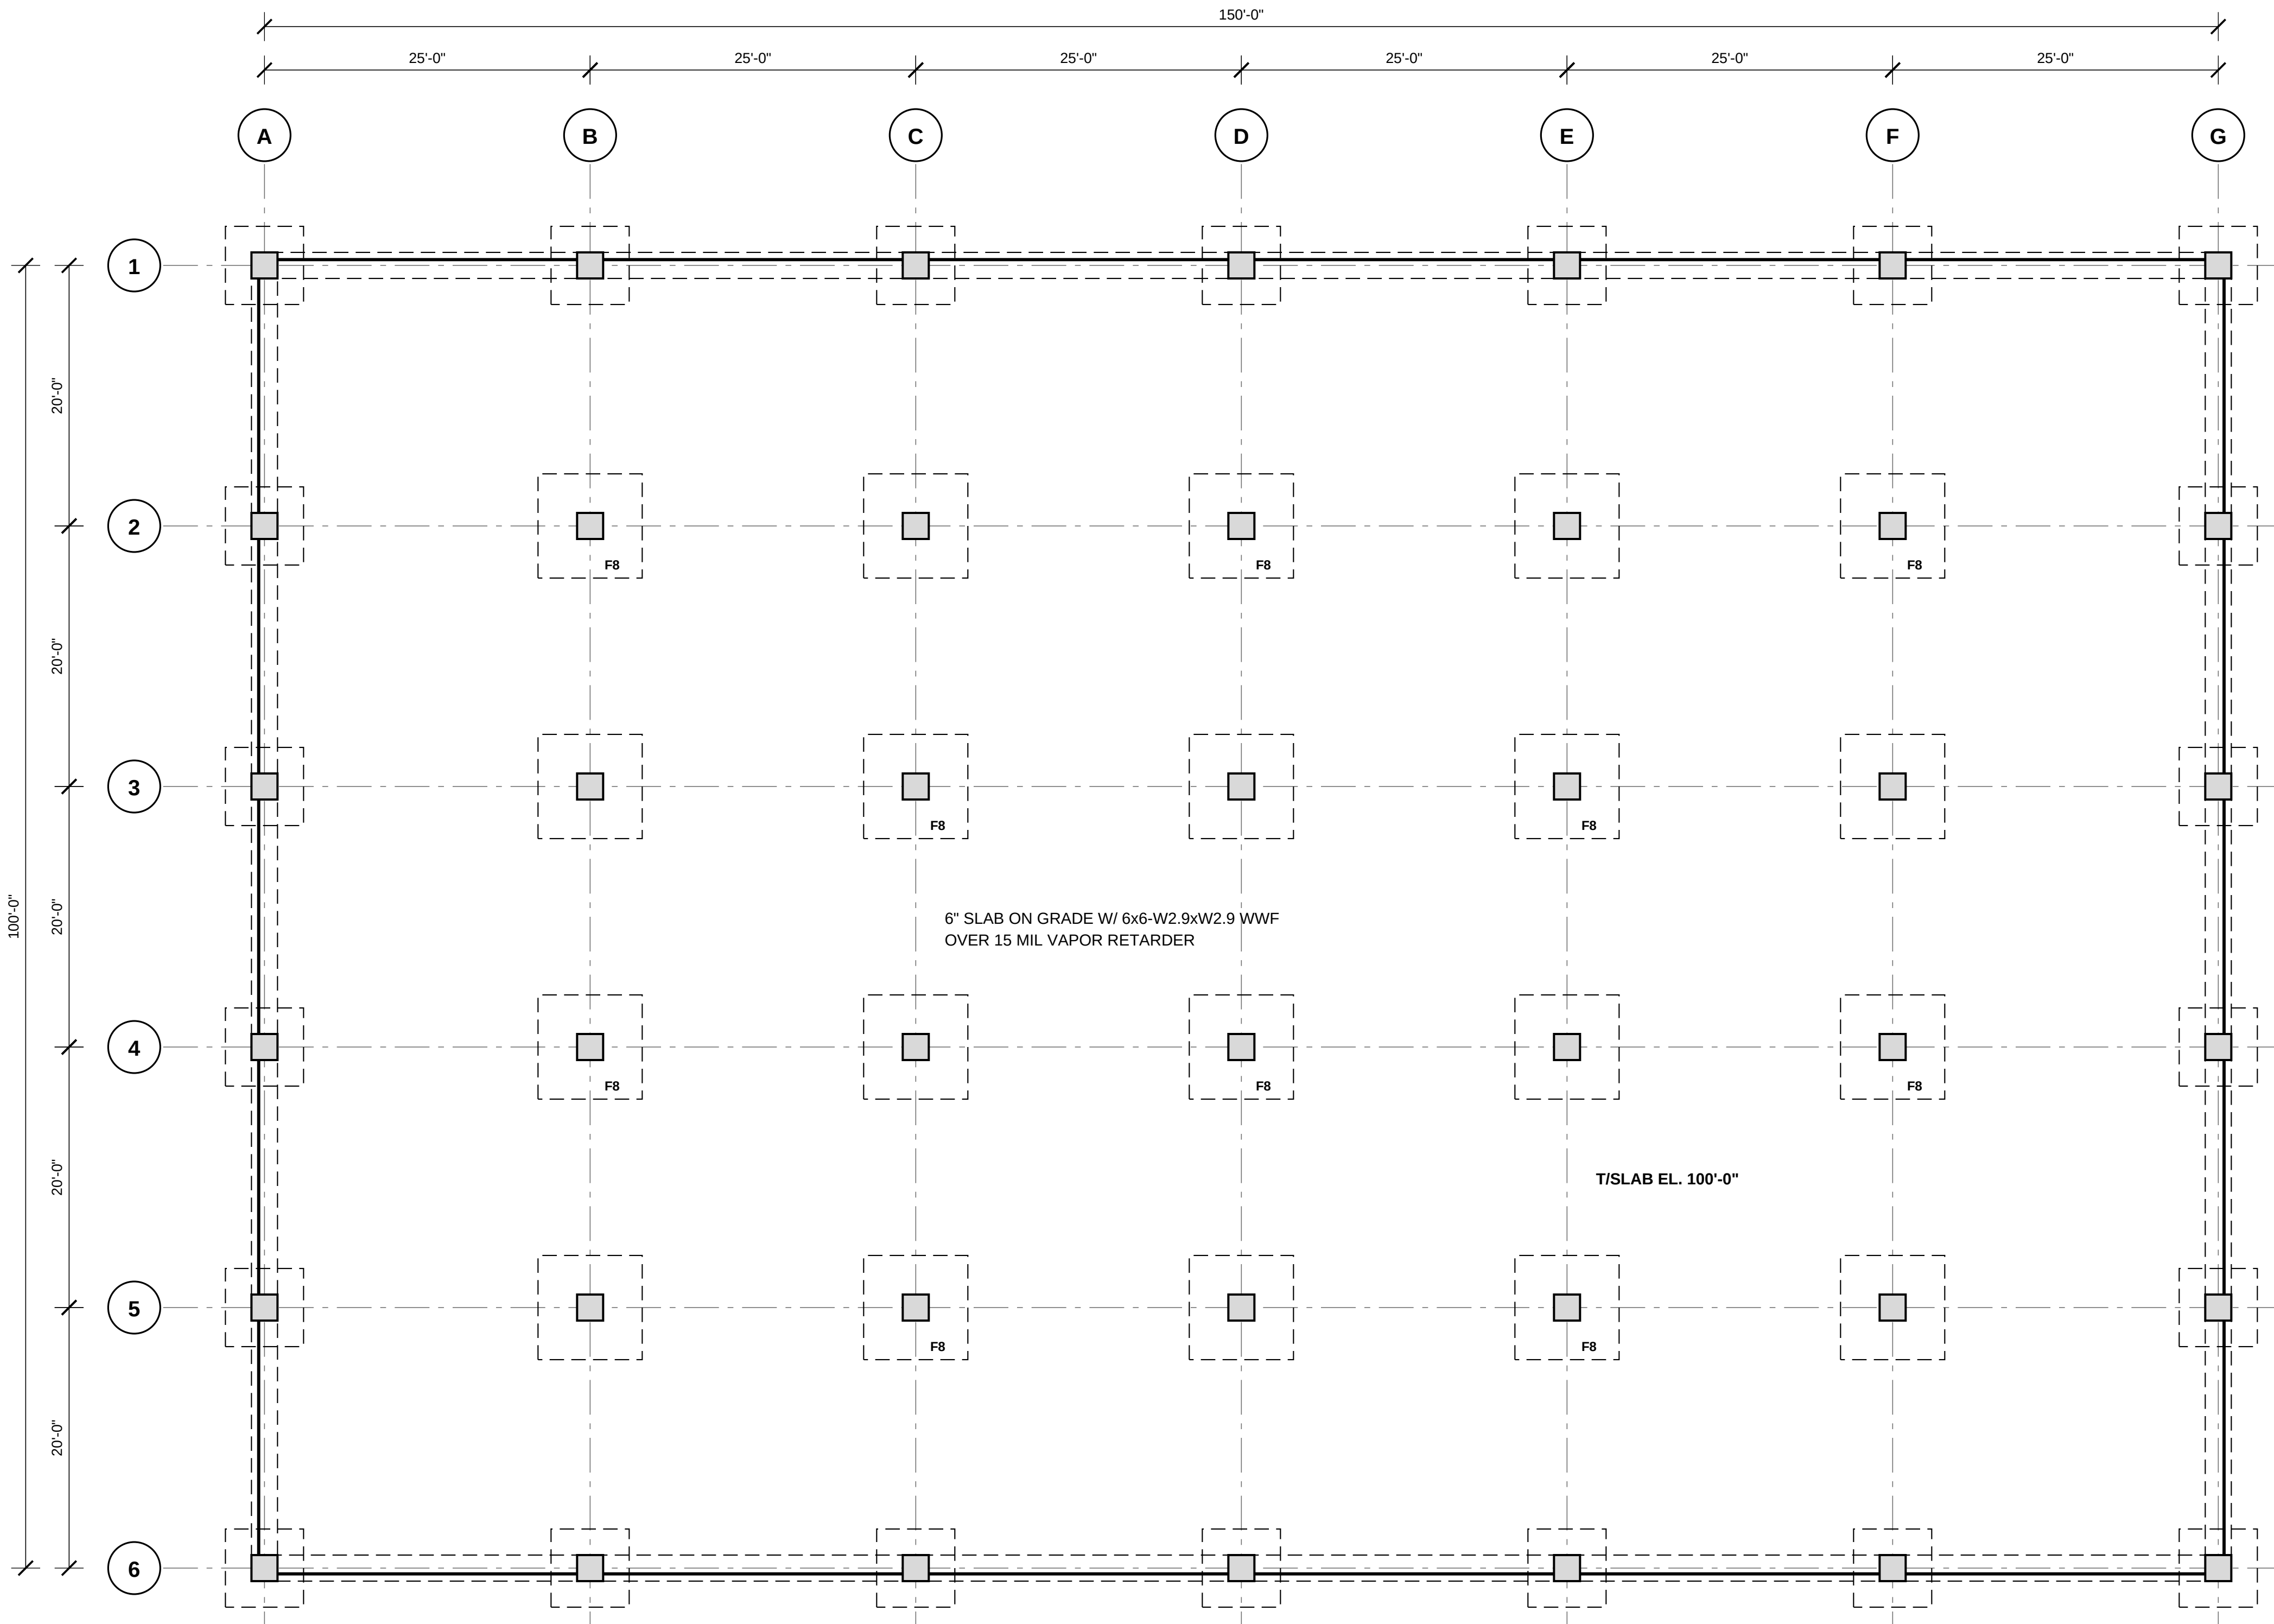

FOOTING SCHEDULE

MARK SIZE REINF.
F6 6'-0" x 6'-0" x 1'-6" (7) #5 E.W.
F8 8'-0" x 8'-0" x 2'-0" (9) #6 E.W.
CF 2'-0" WIDE x 1'-0" (3) #5 CONT.

FOUNDATION NOTES

- ALLOWABLE SOIL BEARING PRESSURE = 3000 PSF.
- CONCRETE: 4000 PSI AT 28 DAYS.
- ANCHOR RODS: ASTM F1554 GR. 36, (4) 3/4" DIA.
- BASE PLATES: PL 3/4" x 12" x 12", ASTM A36.
- GROUT UNDER BASE PLATES: 1 1/2" NON-SHRINK.
- TOP OF FOOTING EL. 97'-0" U.N.O.

1 FOUNDATION PLAN

SCALE: 1/8" = 1'-0"

NORTHPOINT

STRUCTURAL ENGINEERS
1200 Harbor Way, Suite 400

PROJECT

RIVERSIDE
DISTRIBUTION CENTER
4410 Industrial Parkway

REVISIONS


1	ISSUED FOR BID	03/14/2026
2	ADDENDUM 1	04/02/2026

FRAMING NOTES

- STRUCTURAL STEEL: W SHAPES ASTM A992; HSS ASTM A500 GR. C.
- ANGLES, CHANNELS AND PLATES: ASTM A36.
- T/STEEL EL. 124'-0" U.N.O.
- JOISTS: SJI K-SERIES, BRIDGING PER SJI.
- ROOF DECK: 1.5" TYPE B, 20 GA, GALVANIZED.
- BEAM CONNECTIONS: SEE 1/S2.01.

MEMBER LEGEND

W24x55 INTERIOR GIRDER
W18x35 PERIMETER BEAM
W30x90 MOMENT FRAME BEAM
HSS6x6x3/8 COLUMN

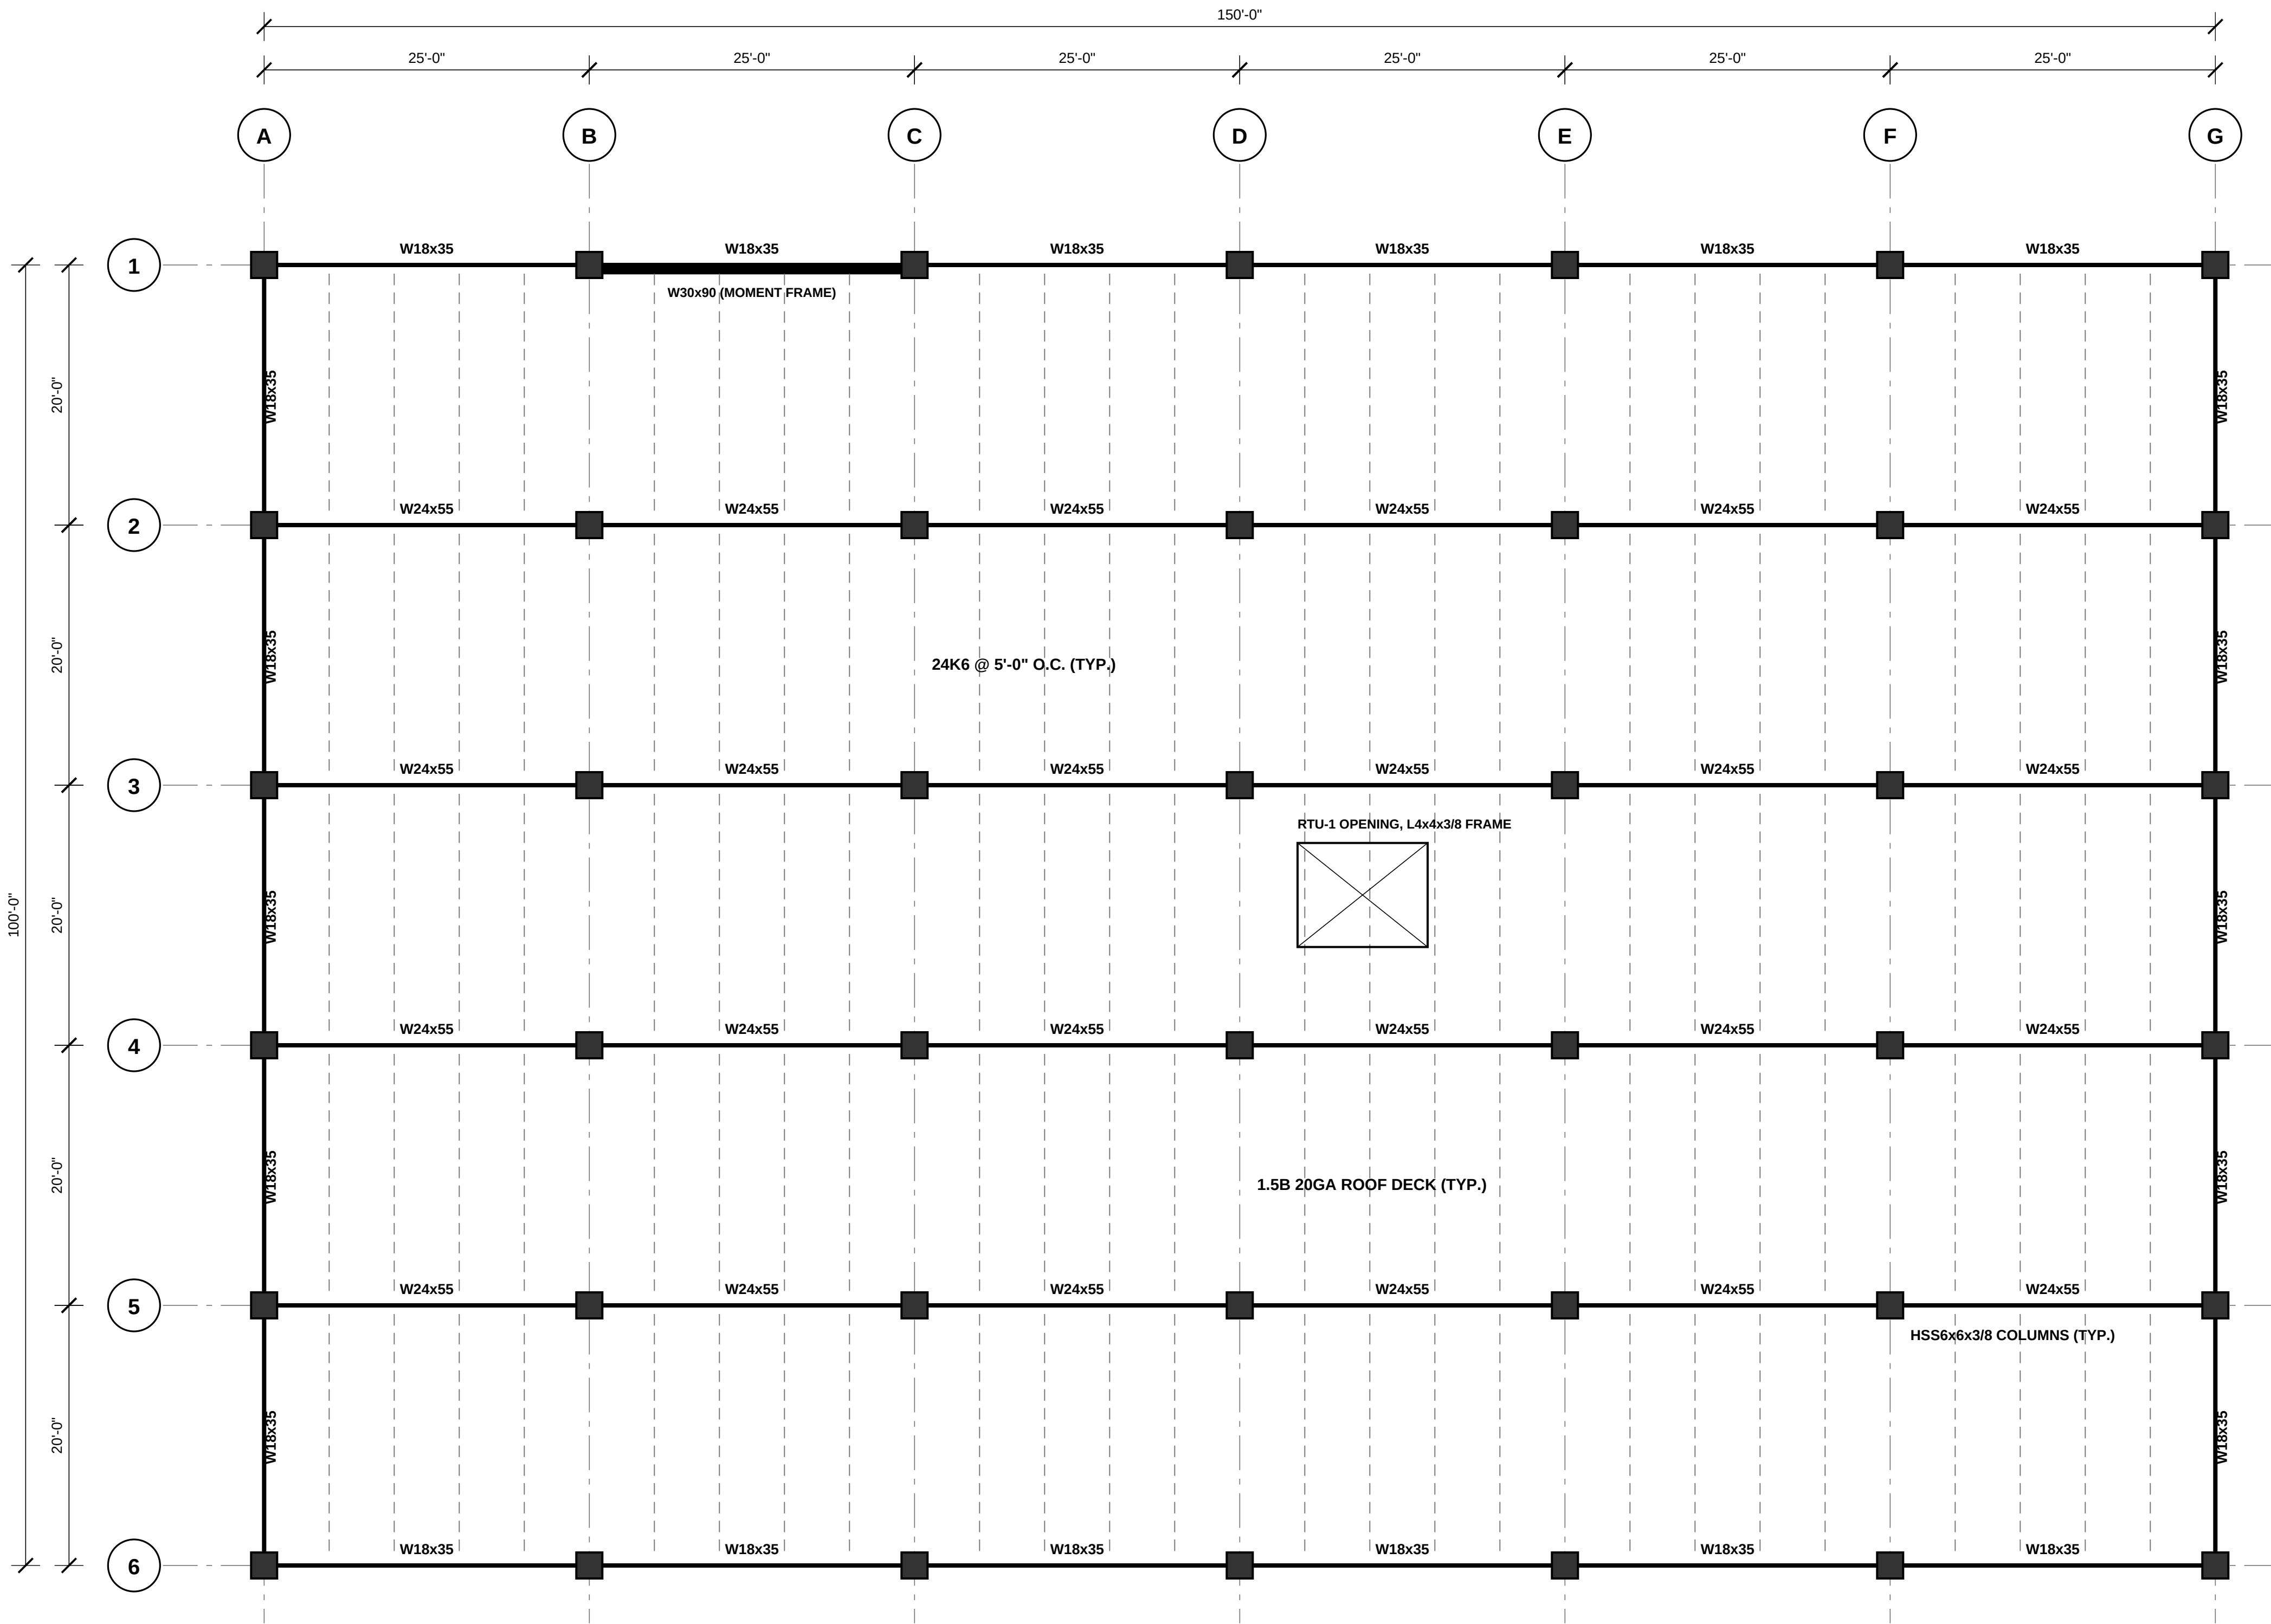

1 ROOF FRAMING PLAN
SCALE: 1/8" = 1'-0"

PROJECT NO.	DATE
2026-118	04/02/2026
DRAWN	CHECKED
JRM	KLT

SHEET TITLE

ROOF FRAMING
PLAN

SHEET NUMBER

S1.02

NORTHPOINT

STRUCTURAL ENGINEERS
1200 Harbor Way, Suite 400

PROJECT

RIVERSIDE
DISTRIBUTION CENTER
4410 Industrial Parkway

REVISIONS

1	ISSUED FOR BID	03/14/2026
2	ADDENDUM 1	04/02/2026

PROJECT NO.

2026-118

DATE

04/02/2026

DRAWN

JRM

CHECKED


KLT

SHEET TITLE

STRUCTURAL
SECTIONS AND
DETAILS

SHEET NUMBER

S2.01

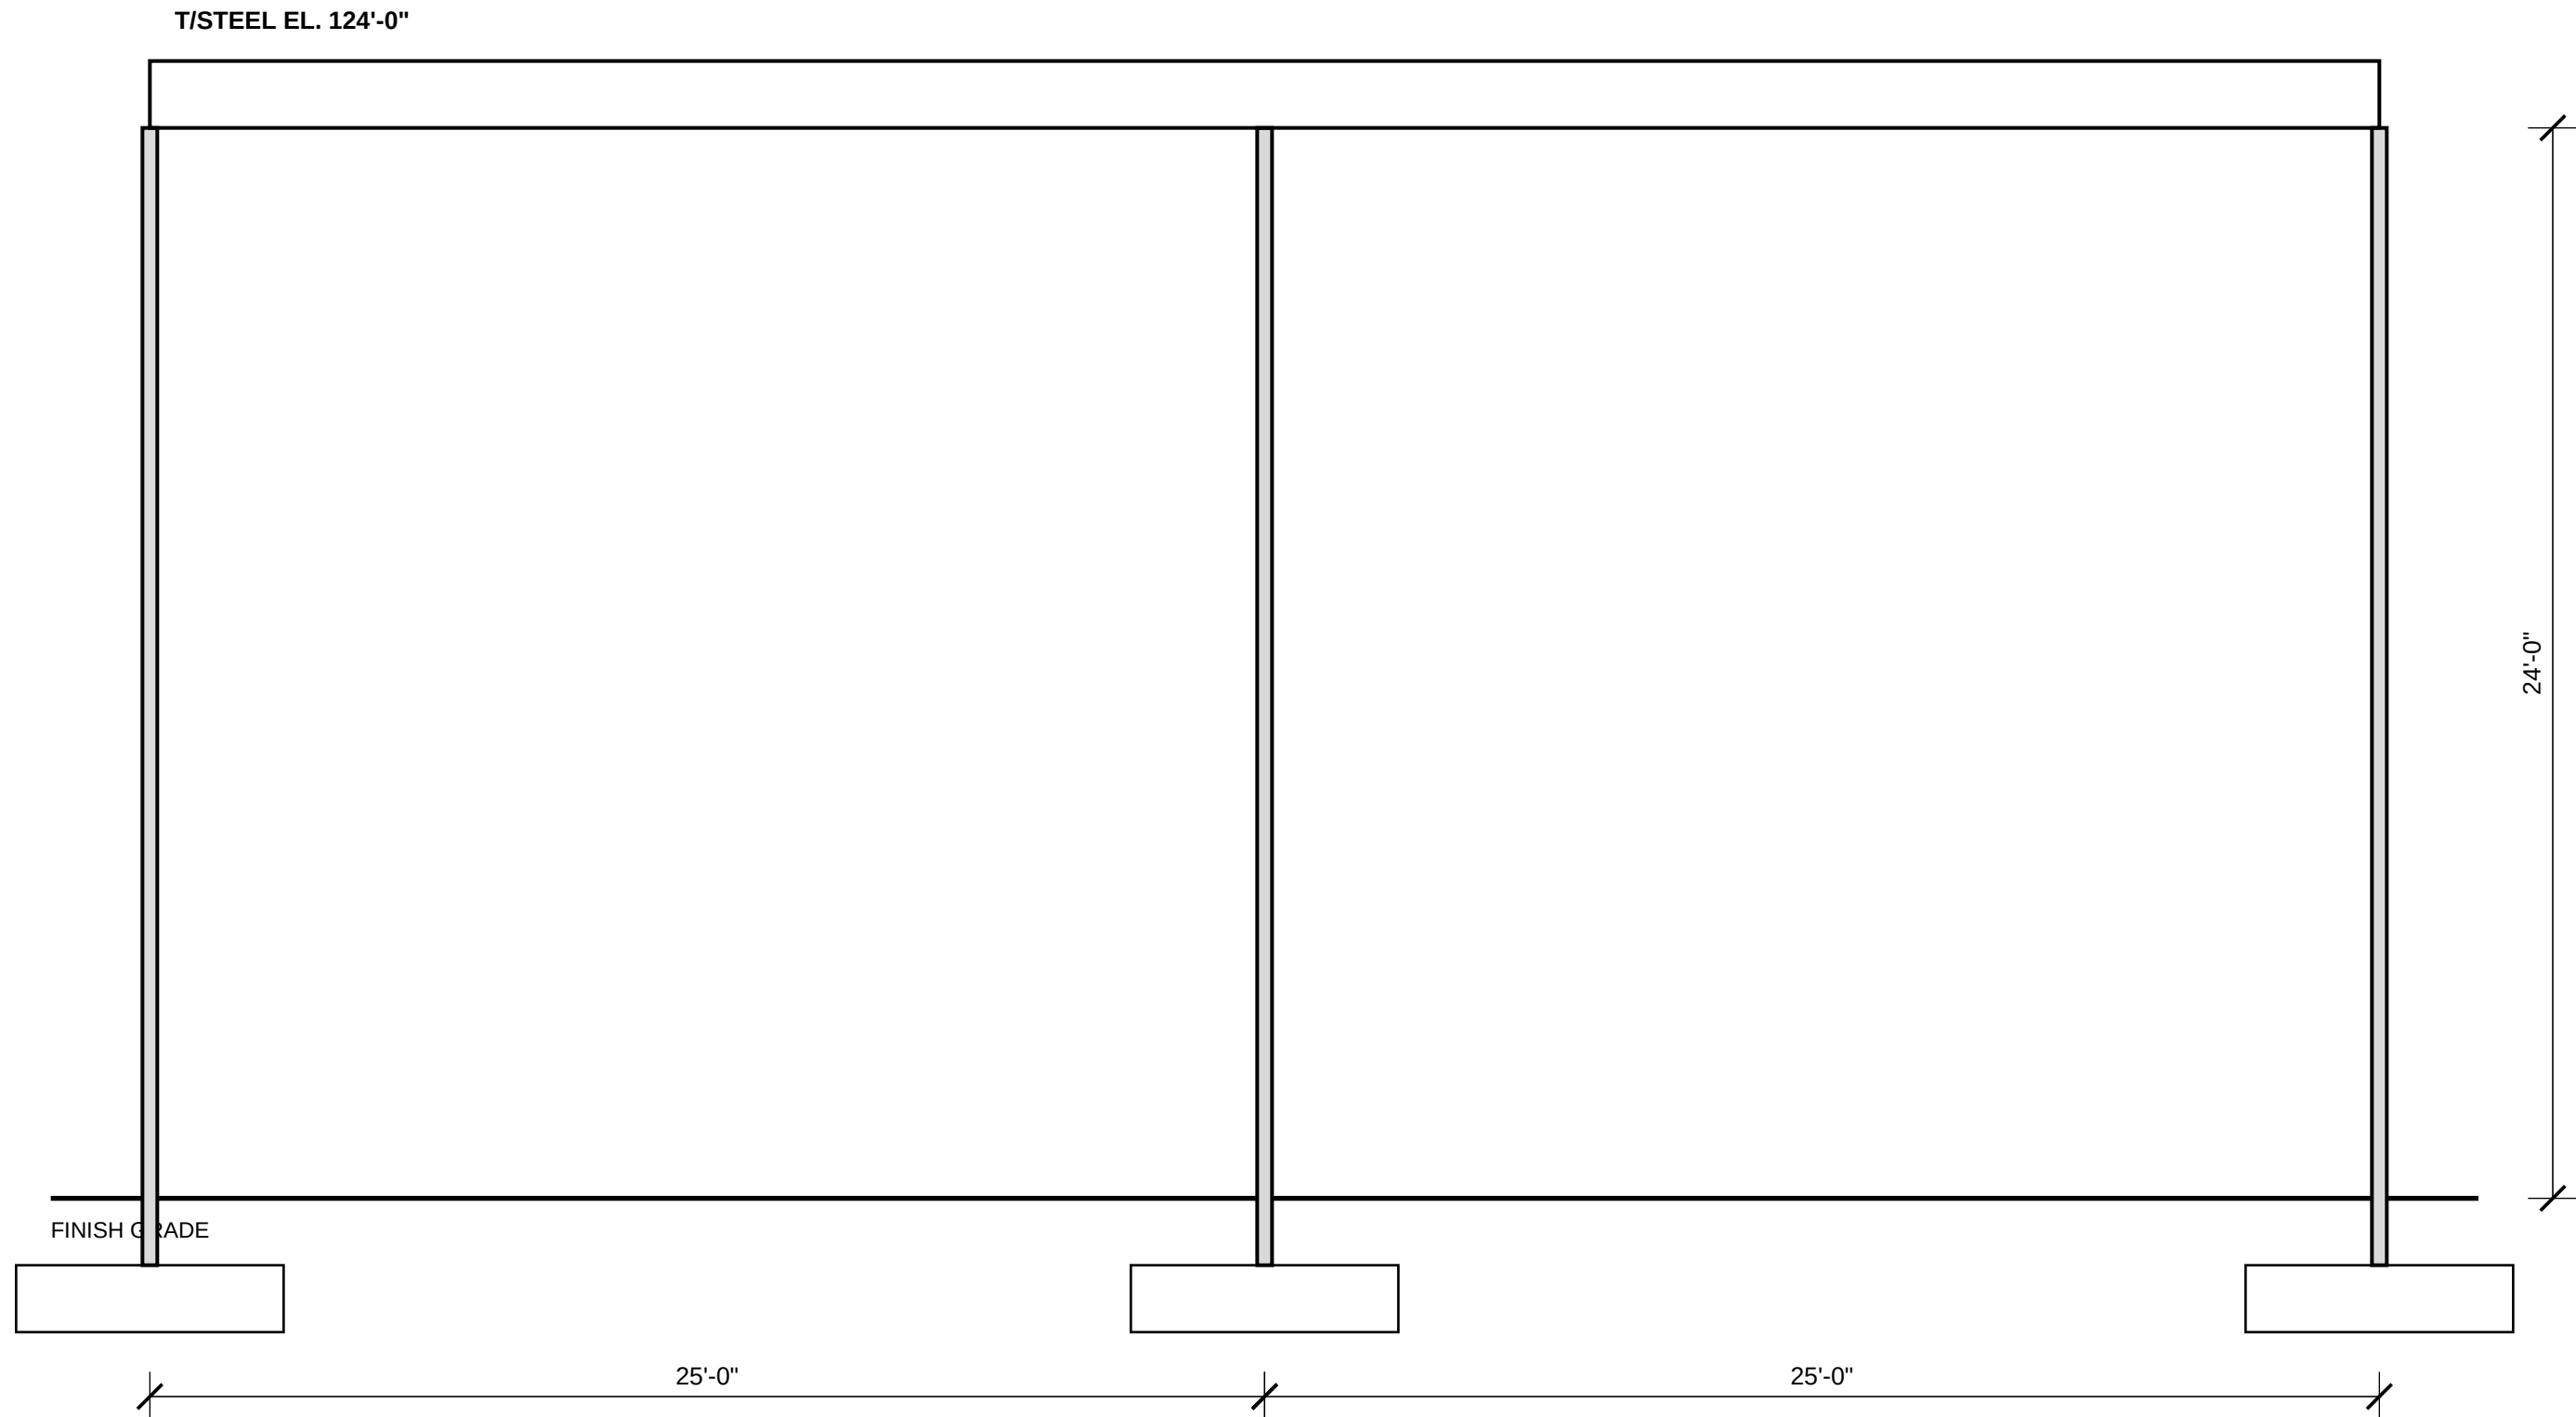


3

BUILDING SECTION

SCALE: 1/4" = 1'-0"

GENERAL NOTES


DETAILS ON THIS SHEET ARE DRAWN AT DIFFERENT SCALES.
CALIBRATE EACH DETAIL (VIEWPORT) INDEPENDENTLY BEFORE MEASURING.

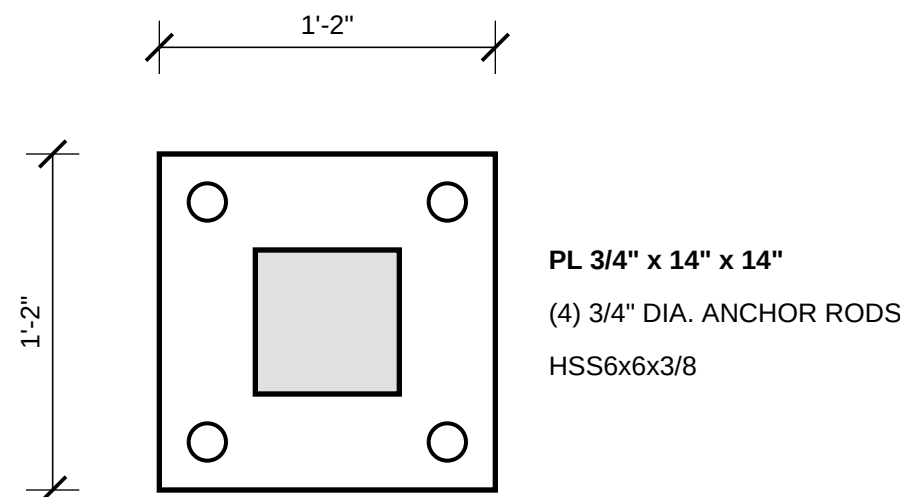

2

COLUMN BASE PLATE


SCALE: 1 1/2" = 1'-0"

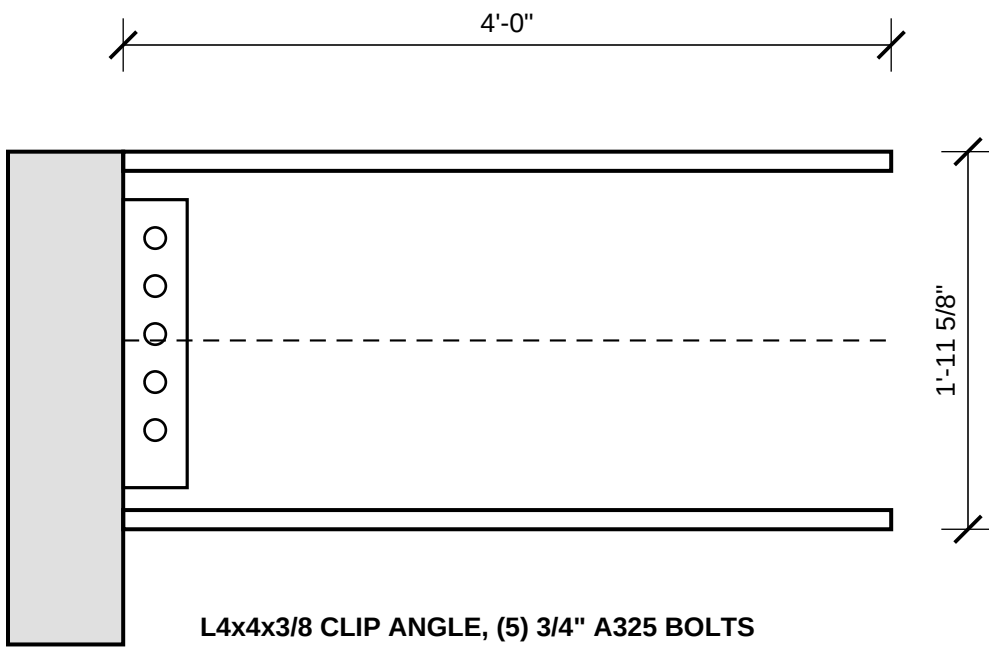

1

TYPICAL BEAM CONNECTION

SCALE: 1" = 1'-0"

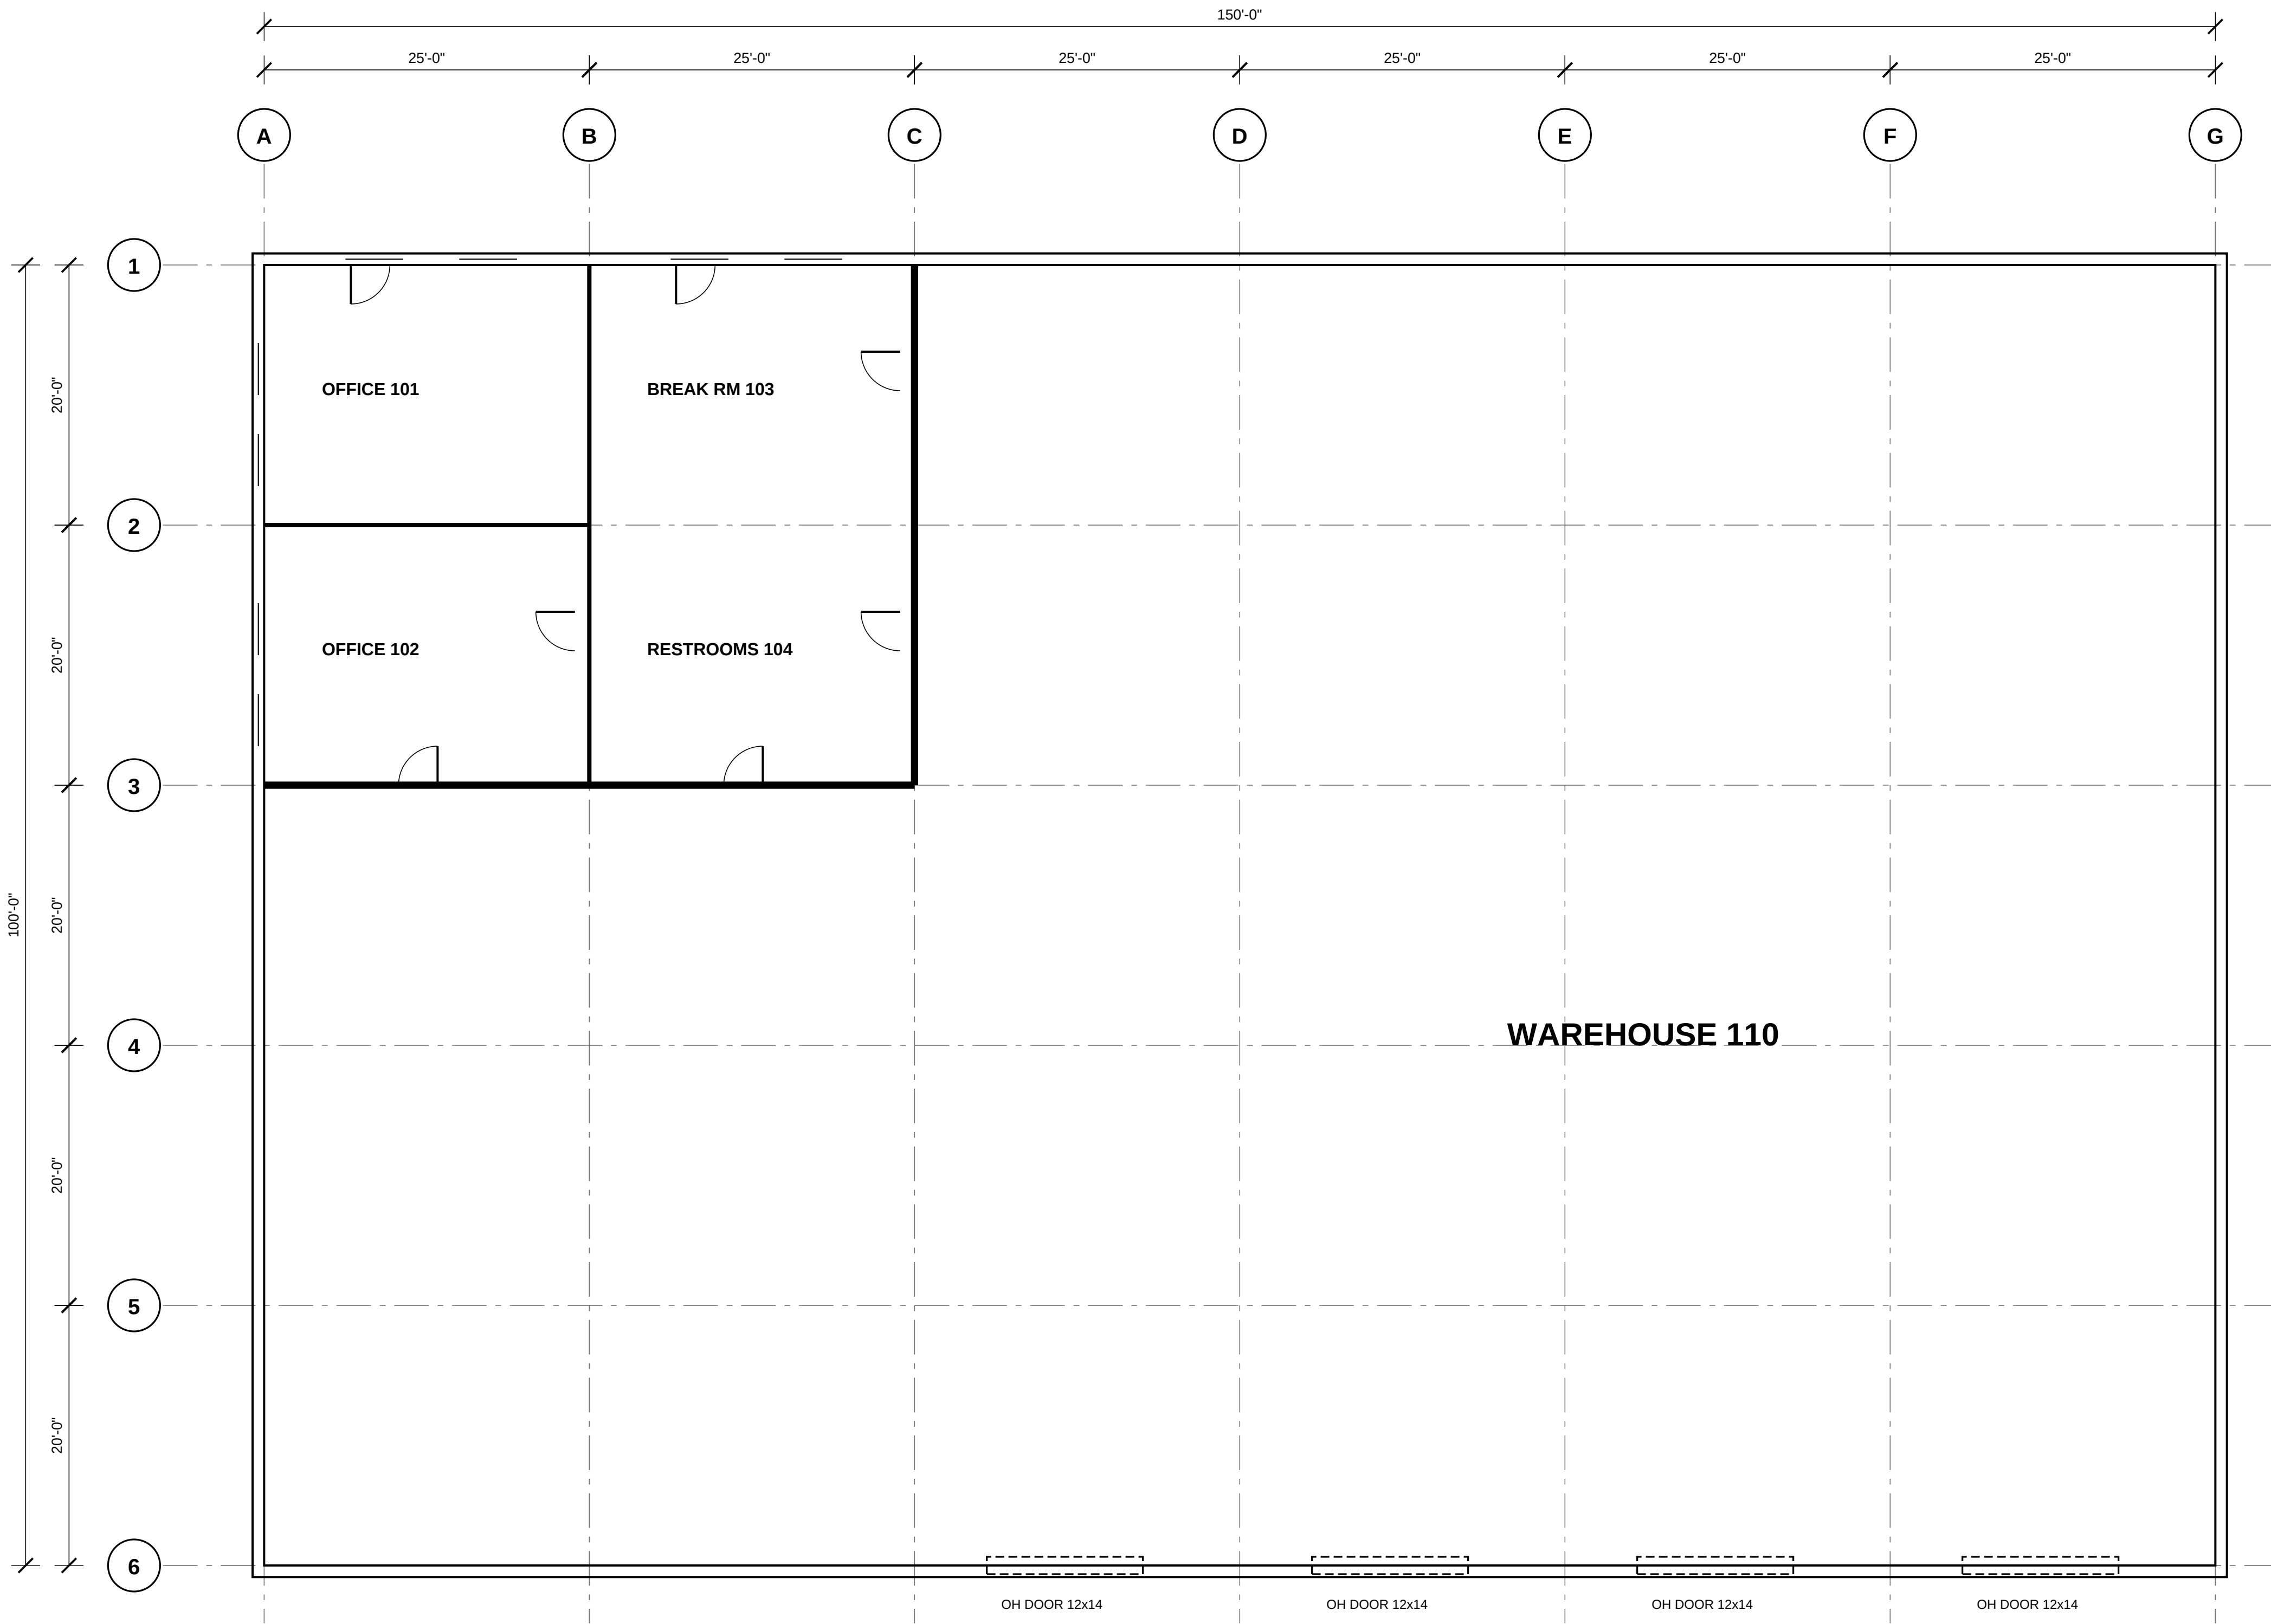

- PLAN NOTES**
- 1. DIMENSIONS ARE TO GRID LINES U.N.O.
 - 2. OFFICE WALLS: 3 5/8" MTL STUD, GYP. BD, EACH SIDE.
 - 3. SEE A6.01 FOR DOOR AND WINDOW SCHEDULES.

1 FIRST FLOOR PLAN
SCALE: 1/8" = 1'-0"

NORTHPOINT
STRUCTURAL ENGINEERS
1200 Harbor Way, Suite 400

PROJECT
RIVERSIDE
DISTRIBUTION CENTER
4410 Industrial Parkway

REVISIONS		
1	ISSUED FOR BID	03/14/2026
2	ADDENDUM 1	04/02/2026

PROJECT NO.	DATE
2026-118	04/02/2026
DRAWN	CHECKED
JRM	KLT

SHEET TITLE
FIRST FLOOR PLAN

SHEET NUMBER

A1.01

NORTHPOINT

STRUCTURAL ENGINEERS
1200 Harbor Way, Suite 400

PROJECT

RIVERSIDE
DISTRIBUTION CENTER
4410 Industrial Parkway

REVISIONS

1	ISSUED FOR BID	03/14/2026
2	ADDENDUM 1	04/02/2026

PROJECT NO.

2026-118

DATE

04/02/2026

DRAWN

JRM

CHECKED


KLT

SHEET TITLE

MECHANICAL AND
PLUMBING PLAN

SHEET NUMBER

M1.01

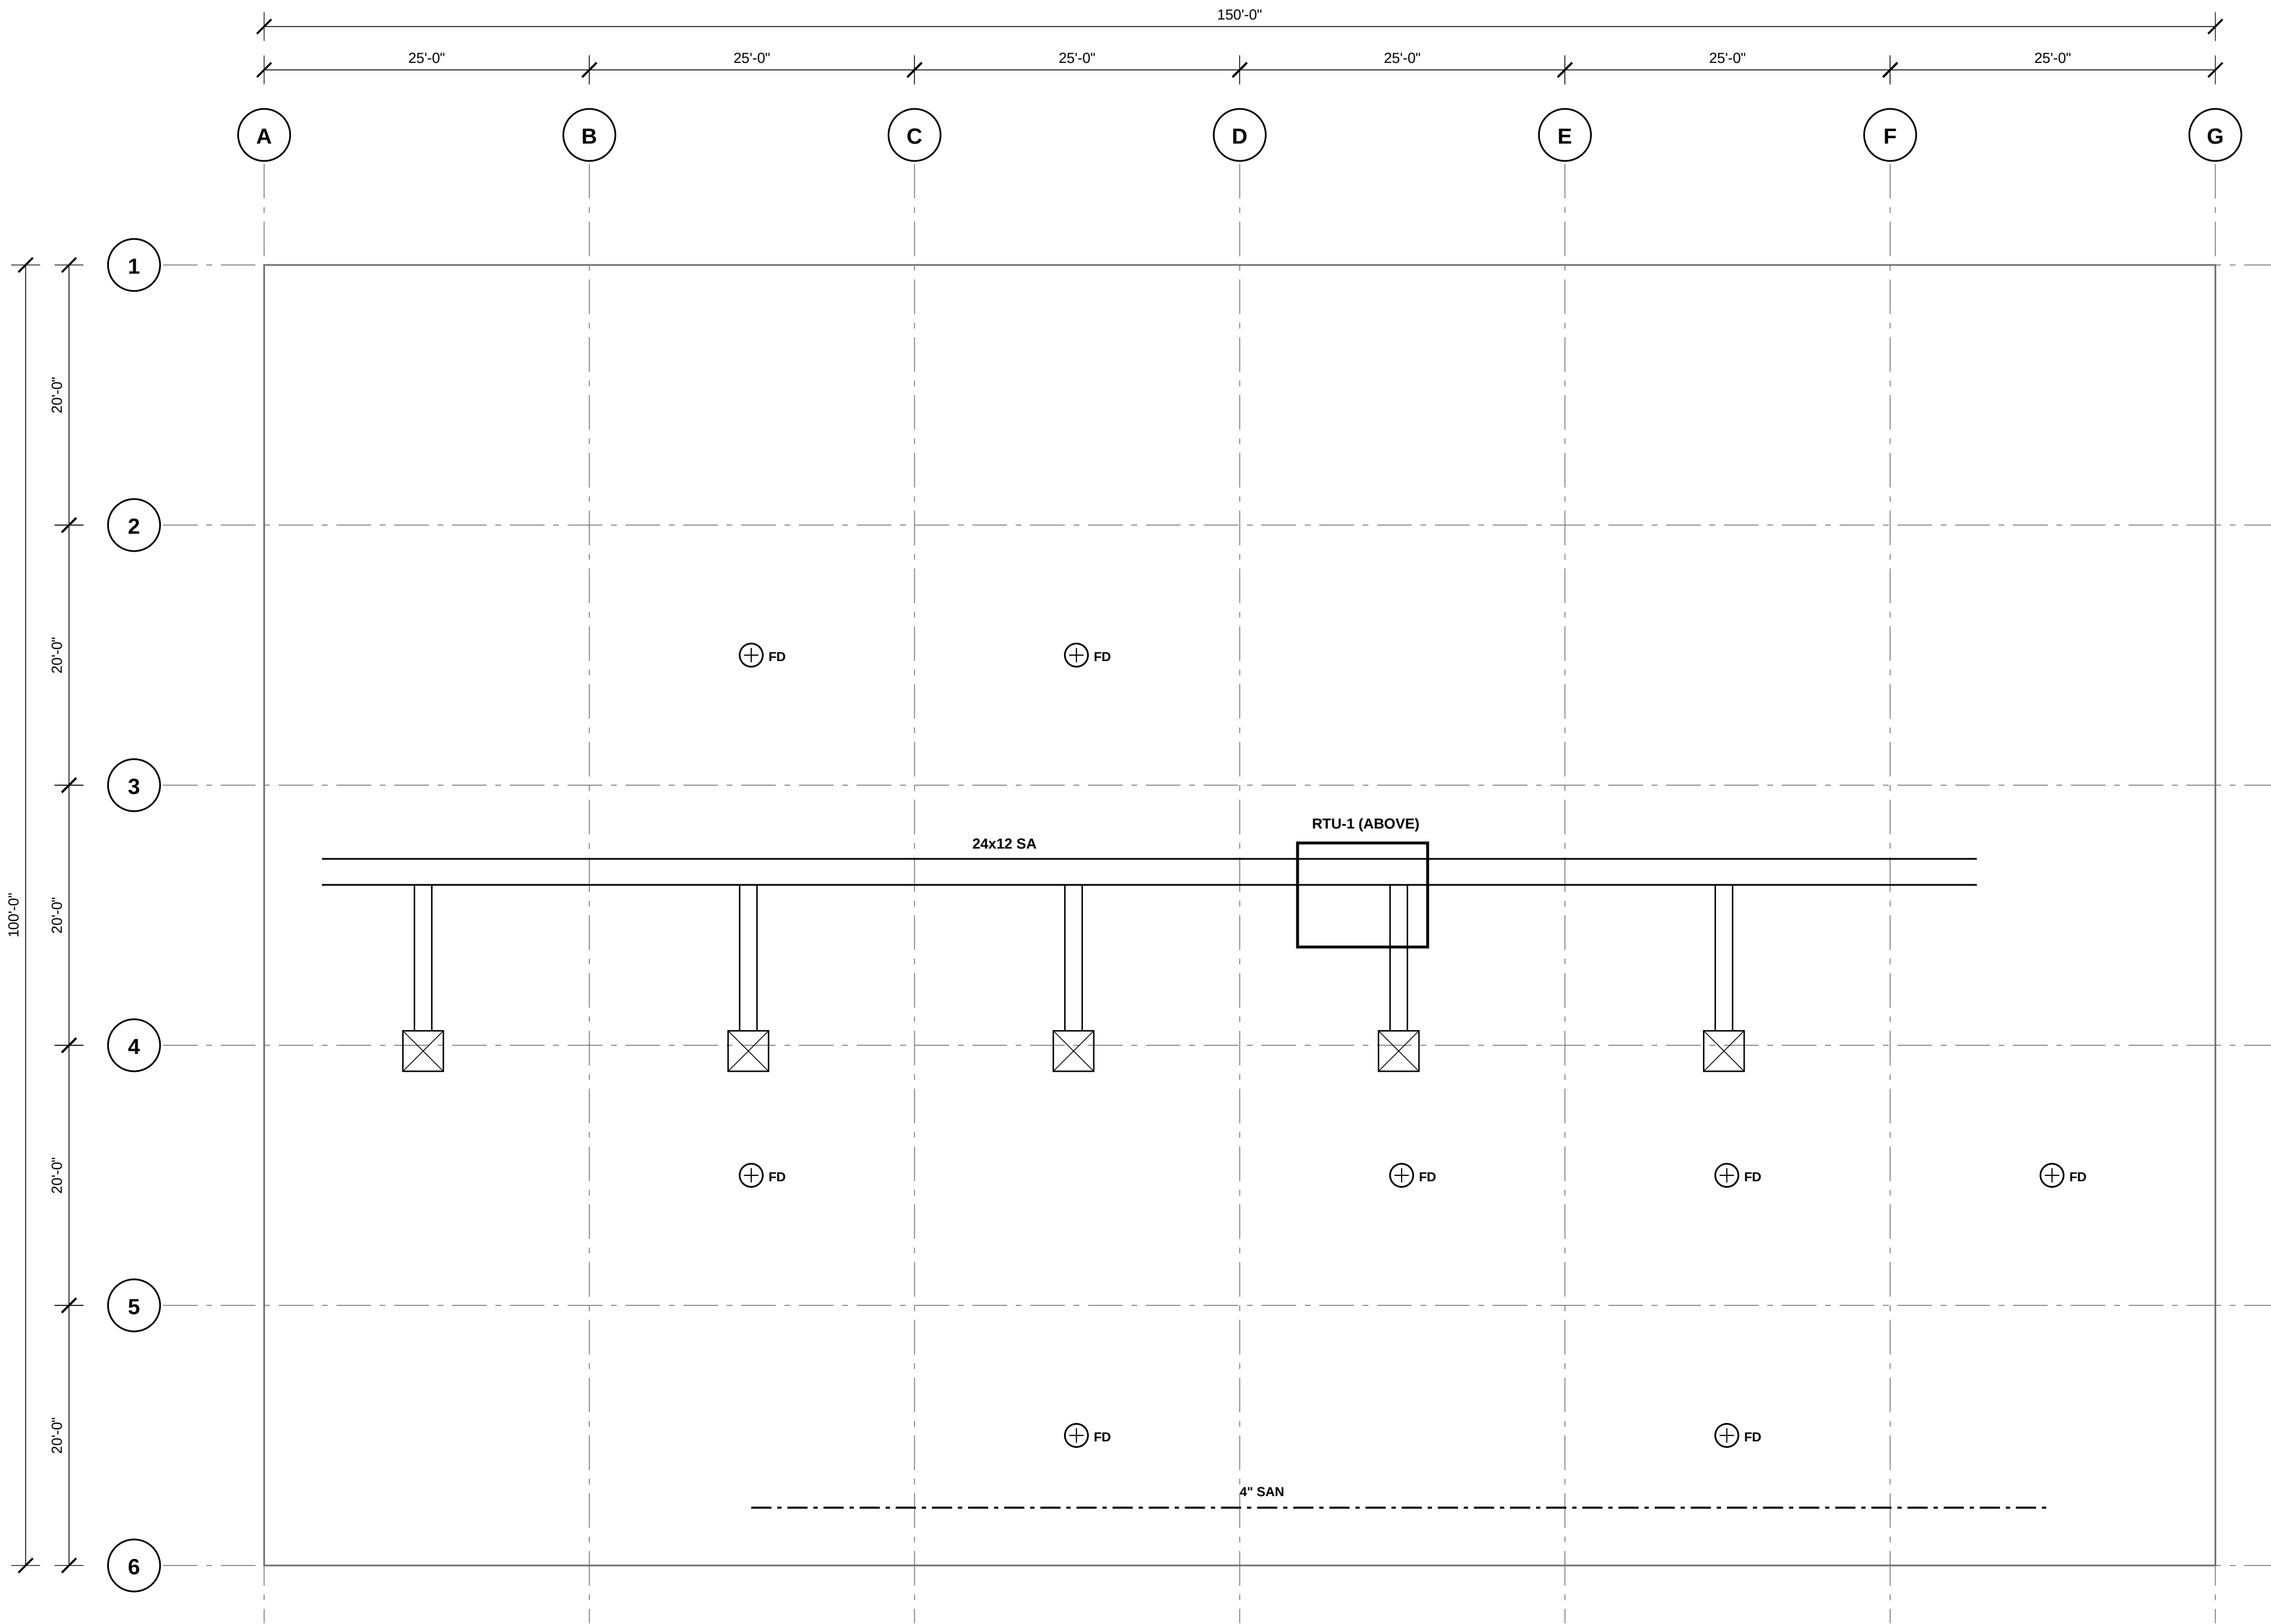

LEGEND

FD FLOOR DRAIN
[X] SUPPLY DIFFUSER 24x24
---- SUPPLY DUCT
- - - SANITARY PIPING

1 MECHANICAL AND PLUMBING PLAN
SCALE: 1/8" = 1'-0"

PROJECT

RIVERSIDE
DISTRIBUTION CENTER
4410 Industrial Parkway

REVISIONS

1	ISSUED FOR BID	03/14/2026
2	ADDENDUM 1	04/02/2026

PROJECT NO.

2026-118

DATE

04/02/2026

DRAWN

JRM

CHECKED


KLT

SHEET TITLE

ELECTRICAL
LIGHTING PLAN

SHEET NUMBER

E1.01

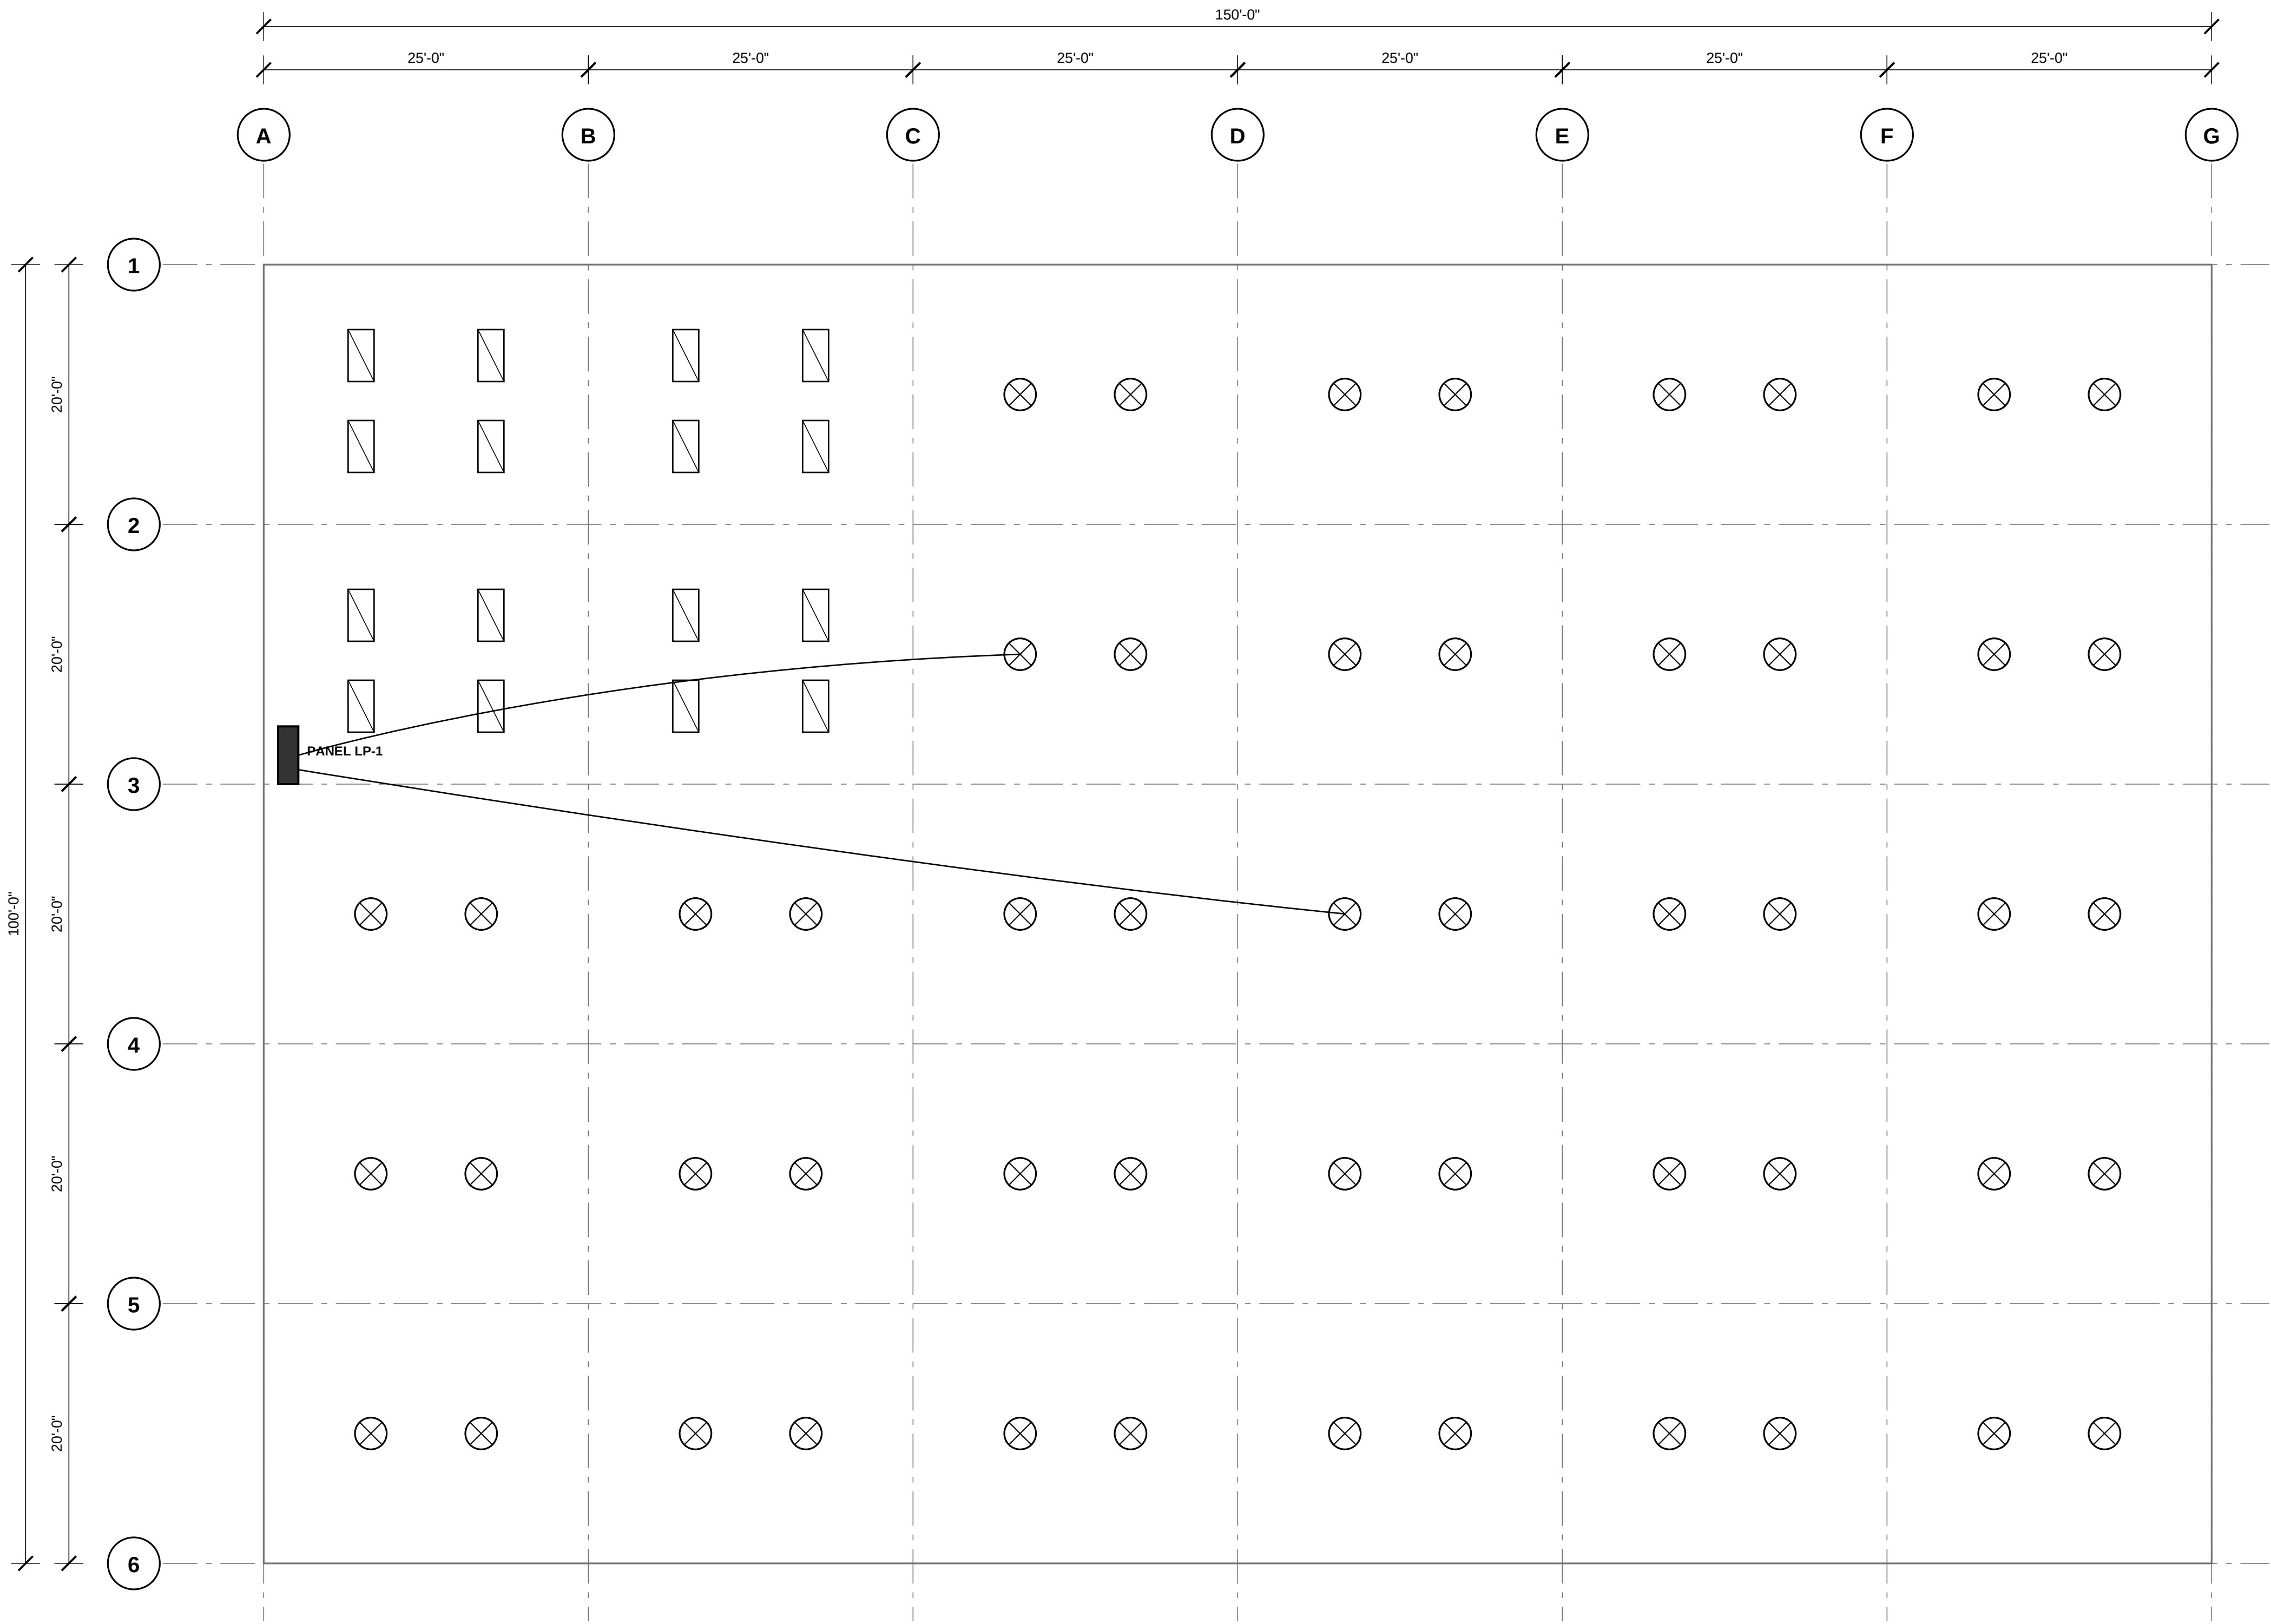

FIXTURE SCHEDULE

TYPE A 2x4 LED TROFFER (OFFICES)
TYPE B LED HIGH BAY 24,000 LM (WAREHOUSE)
ALL FIXTURES ON LP-1, 277V.

1 ELECTRICAL LIGHTING PLAN

SCALE: 1/8" = 1'-0"